

Графическая фиксация нарушений на чертежах

Сопоставлены проектная документация АНО/150321/1-П-ИОС5.4.2 и рабочая документация АНО/150321/1-РД-ОВ1, АНО/150321/1-РД-ОВ2.1. Разметка показывает конкретные зоны, подтверждающие три пункта предоставленного перечня нарушений.

№	Объект сравнения	ПД	РД	Выявленное расхождение
1	Венткамера 012	Лист 26	ОВ1, лист 3	Конфигурация приточных установок и подключений отличается от проектной.
2	Помещения МГН 267, 270, 271, 272	Лист 21	ОВ2.1, лист 4	В ПД показаны контуры теплого пола; в РД они отсутствуют.
3	Помещения 140, 142, 147, 198, 314	Лист 10	ОВ1, листы 4 и 6	Для 140/142 отсутствуют проектные локальные вытяжные ветви; для 147/198/314 конфигурация изменена.

- ПД - проектное решение, база сравнения
- РД - зона отсутствующего или измененного решения

Все выводы относятся к указанным листам и зонам. Рамка вокруг помещения не означает нарушение всего листа.

Конфигурация приточных установок не соответствует проектной документации

The diagram illustrates a heating system layout. A central horizontal pipe at the top is labeled T12. A vertical pipe on the left is labeled T22. The system includes several radiators, each with a pump symbol (a circle with a dot) and a valve symbol (a rectangle with a diagonal line). The radiators are labeled with numbers: П2, П9, П8, П15, П10, П2.1, П18, and П17. The system is divided into two main sections: 'Венткамера' (Ventilation chamber) and 'Формкамера' (Forming chamber). The 'Формкамера' section is further labeled with '012.1'. The diagram also shows a section labeled 'В' and a section labeled 'По'.

кВт, U=3x380 В

AMH-K 300x100
L 220

SBOW 60-35/143, 9 л/с

Чэл.=0,68 кВт, U=1x230 В

П2.1, П8, П18
П3, П10, П15

0x350

350

200x200

400x400

450x350

600x350

0

Ø160

Ø160

11

14

Е130

В2

П17.1, 17.2

012

013

1200x350

800x400

450x300

500x300

200x200

550x300

750x300

500x1000

650x250

19

17

6

3

12

11

28

400x300

600x400


М.С. 19x19*0,8 мм
L 3320

Страница 2

Нарушение 2. Помещения МГН 267, 270, 271 и 272


Проектные контуры теплого пола отсутствуют в рабочей документации

ПД - лист 21

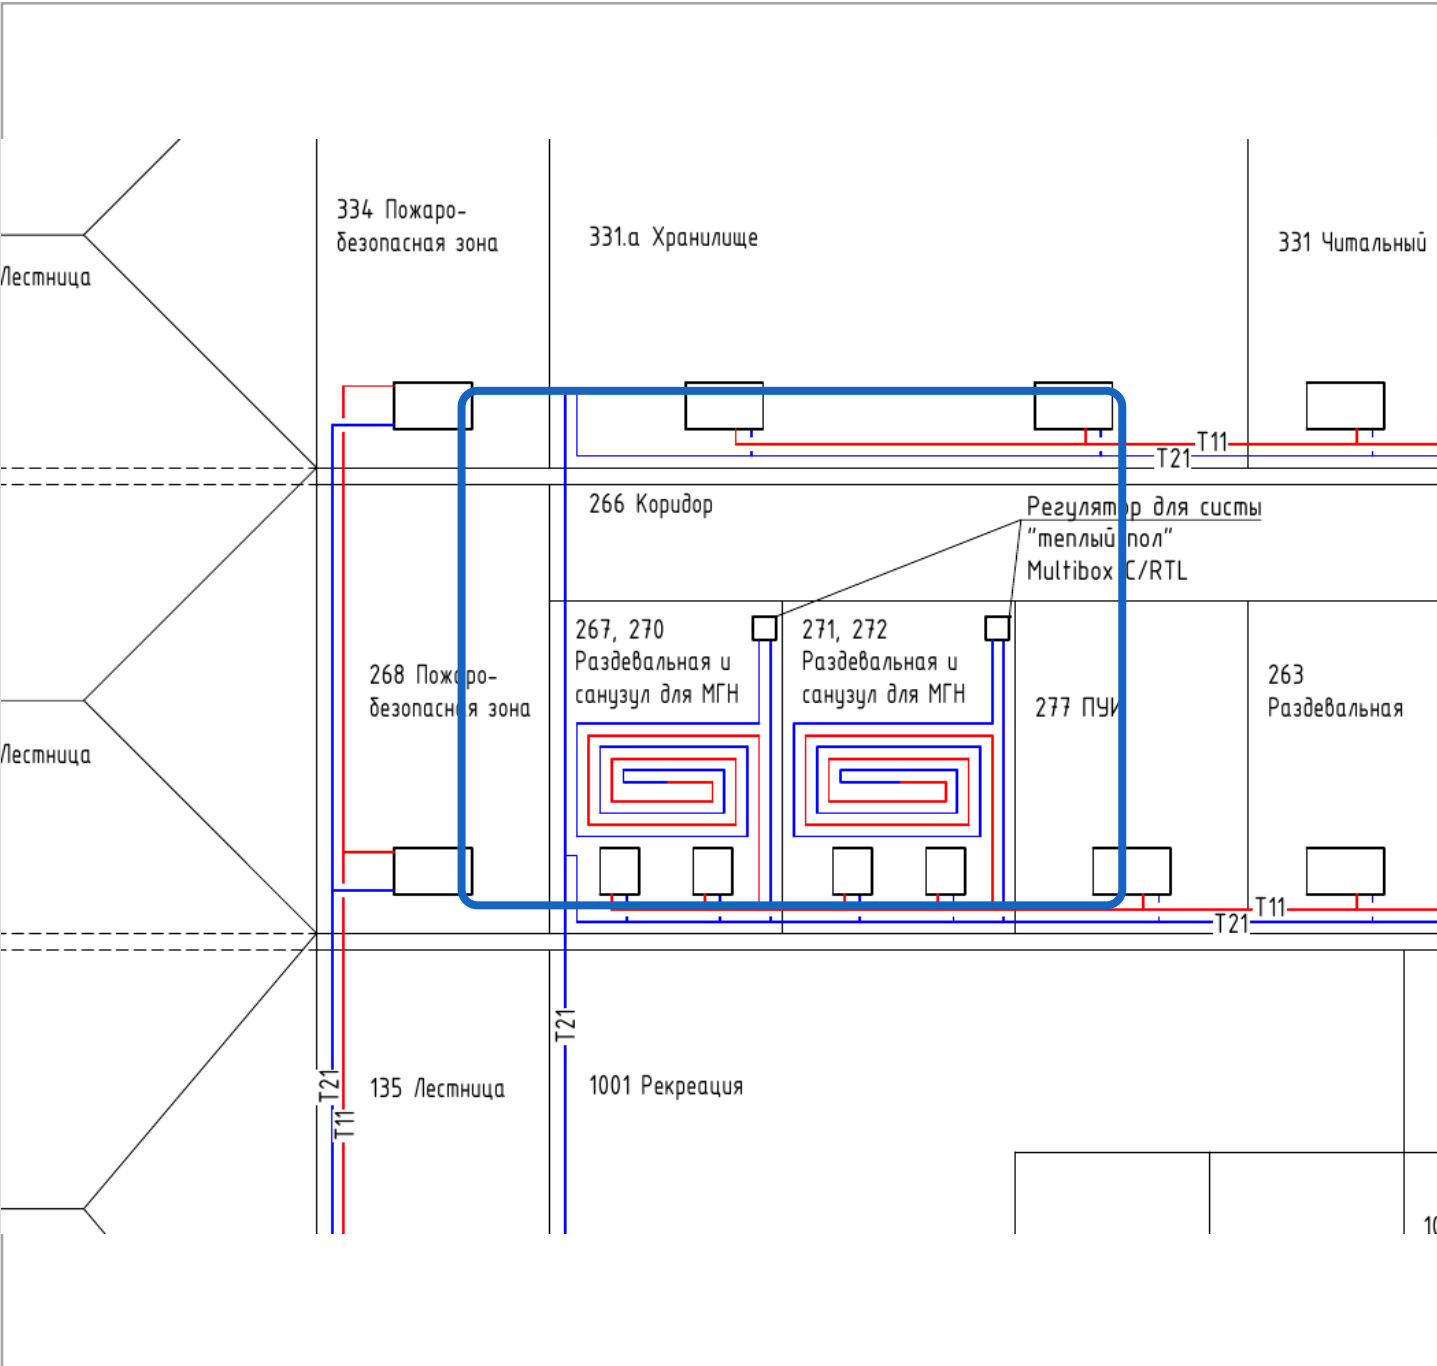

В помещениях 267/270 и 271/272 показаны два самостоятельных контура теплого пола.

РД ОВ2.1 - лист 4

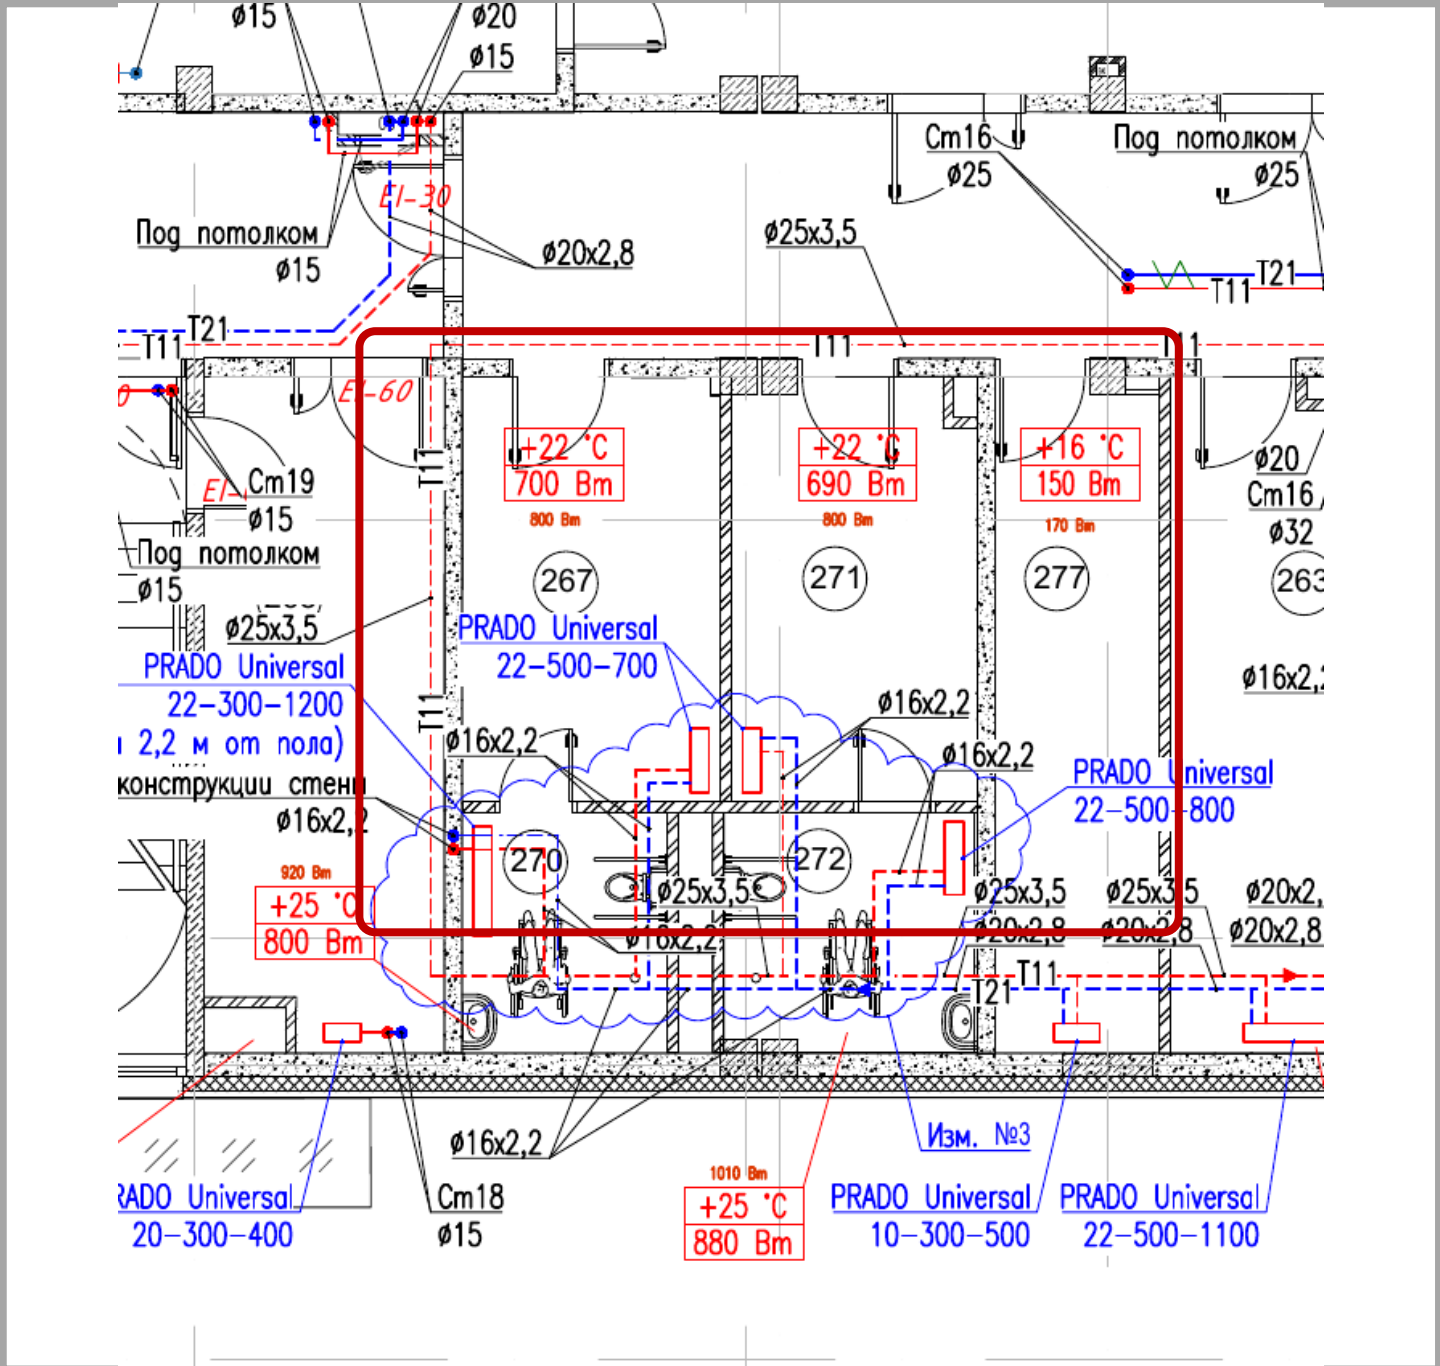


Показаны отопительные приборы и разводка; условные обозначения контуров теплого пола отсутствуют.

Вывод
Работы по устройству предусмотренной ПД системы теплых полов для четырех помещений МГН в РД не отражены.

Нарушение 3. Помещения 140 и 142


Отсутствуют проектные локальные вытяжные ветви

ПД - лист 10

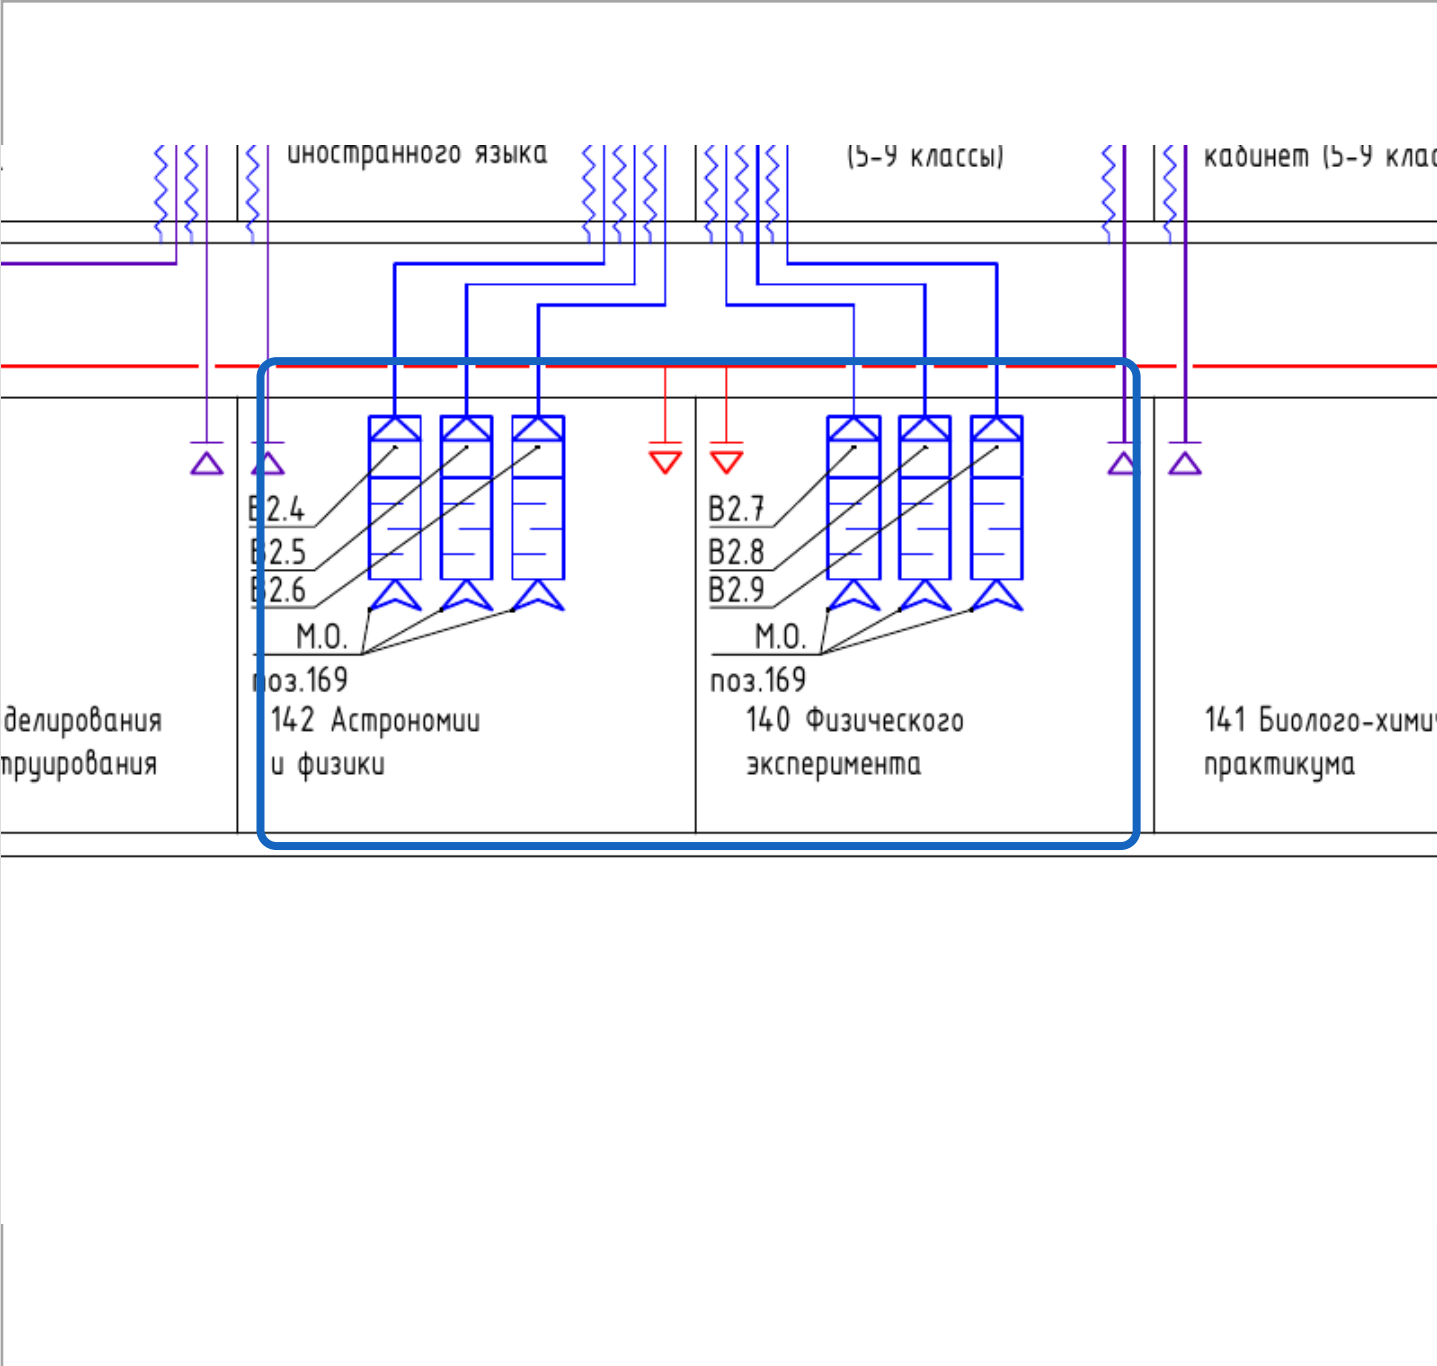

Для 142 предусмотрены ветви B2.4-B2.6; для 140 - B2.7-B2.9, по три местных отсоса.

РД ОВ1 - лист 4

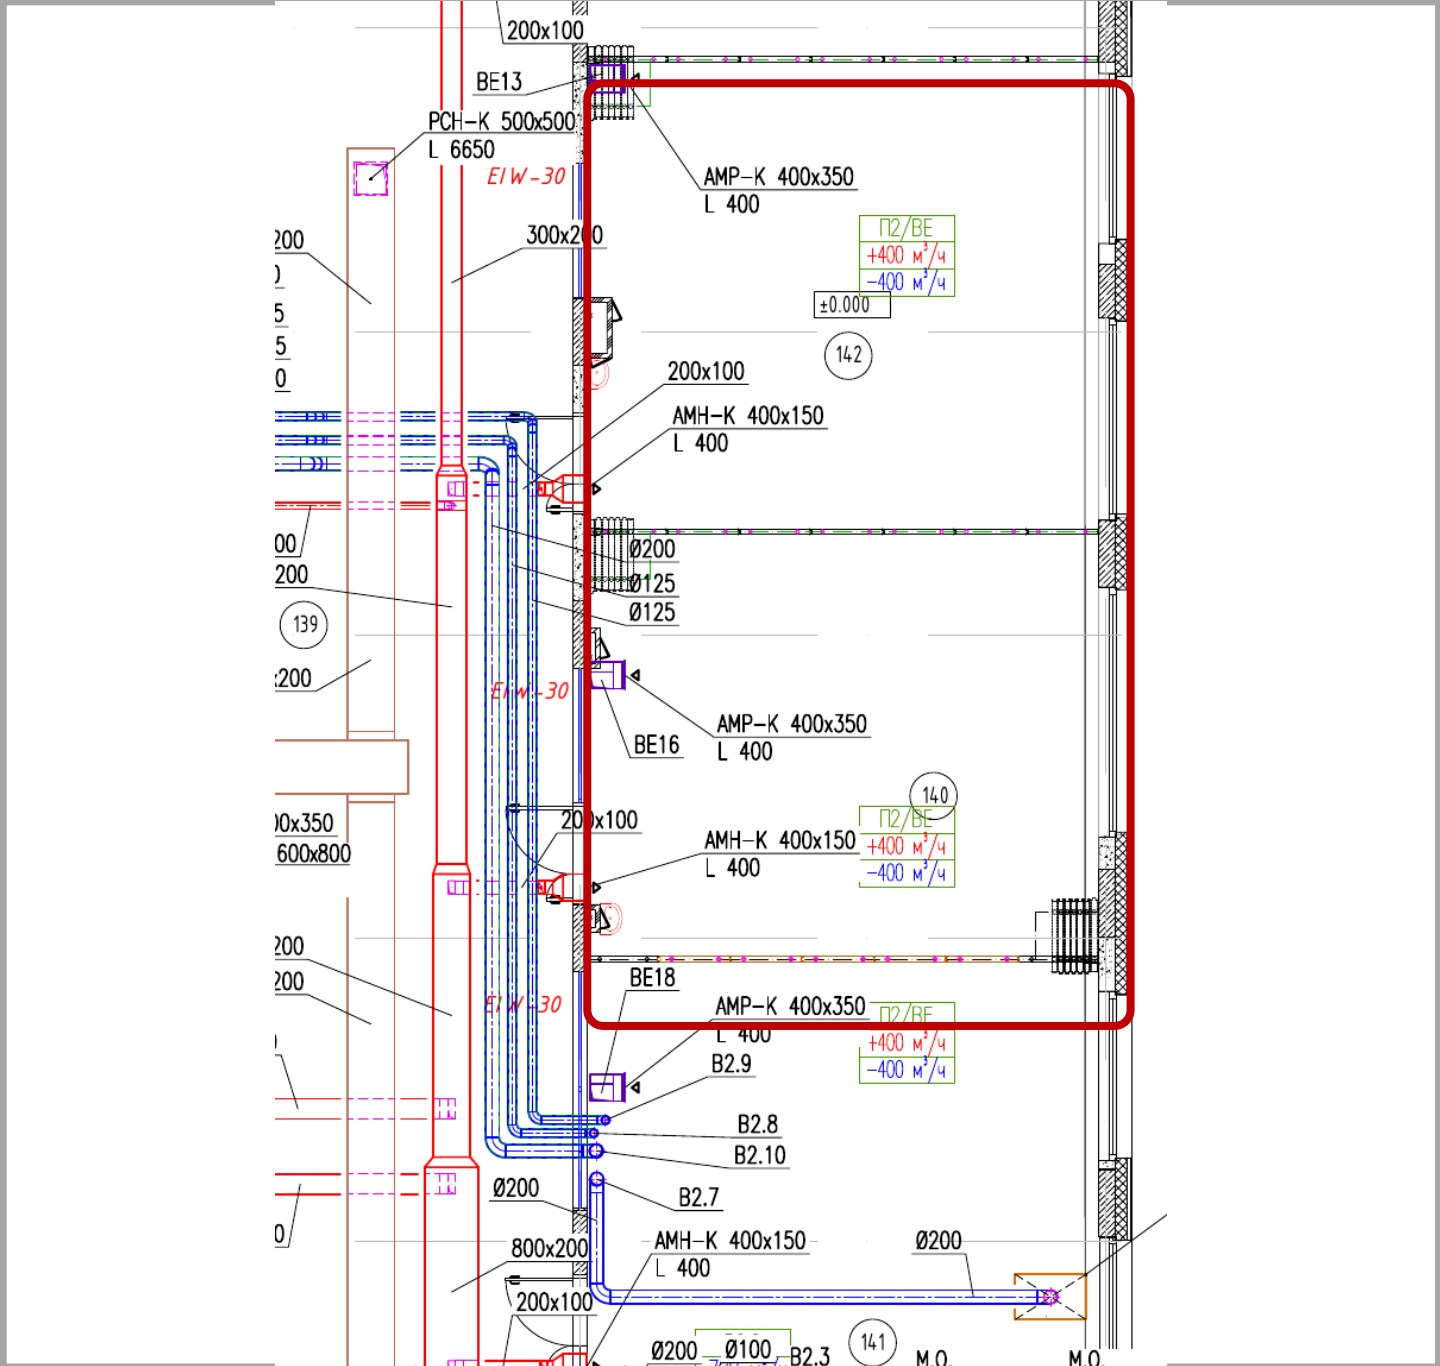

В помещениях показан общеобмен П2/ВЕ; проектные группы местных отсосов внутри 140 и 142 не показаны.


Вывод

Нарушение относится к отсутствию проектных локальных вытяжек, а не к полному отсутствию общеобменной вентиляции.

Нарушение 3. Помещения 147 и 198


Конфигурация вытяжной вентиляции изменена

ПД 147 - лист 10

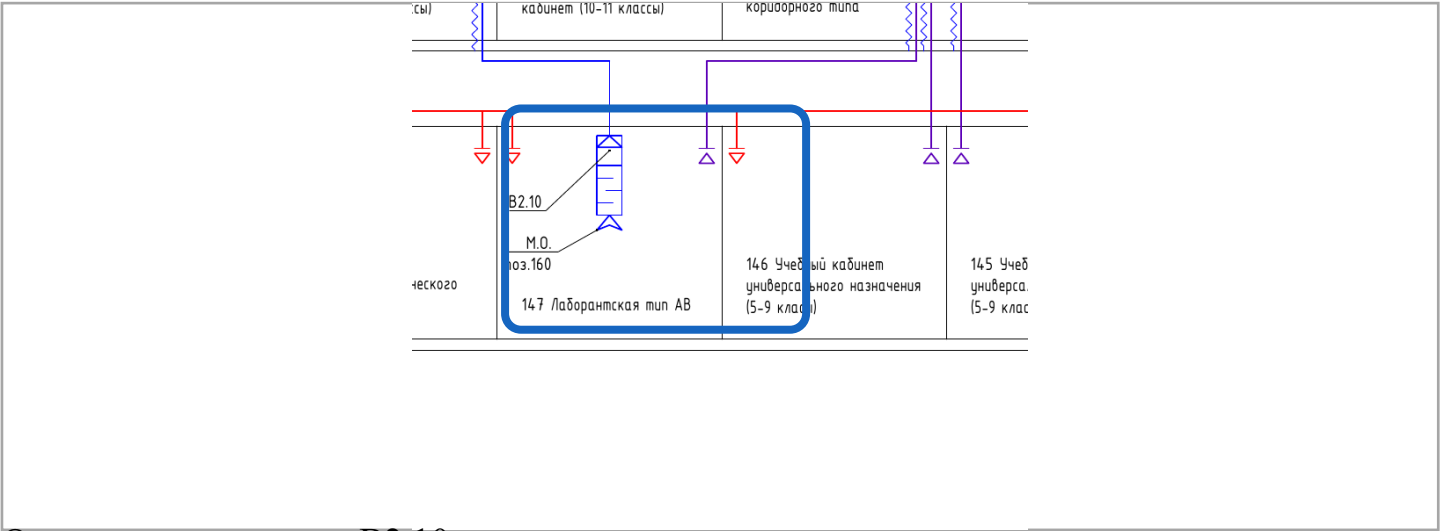


Одна проектная ветвь В2.10 к местному отсосу.

РД 147 - лист 4

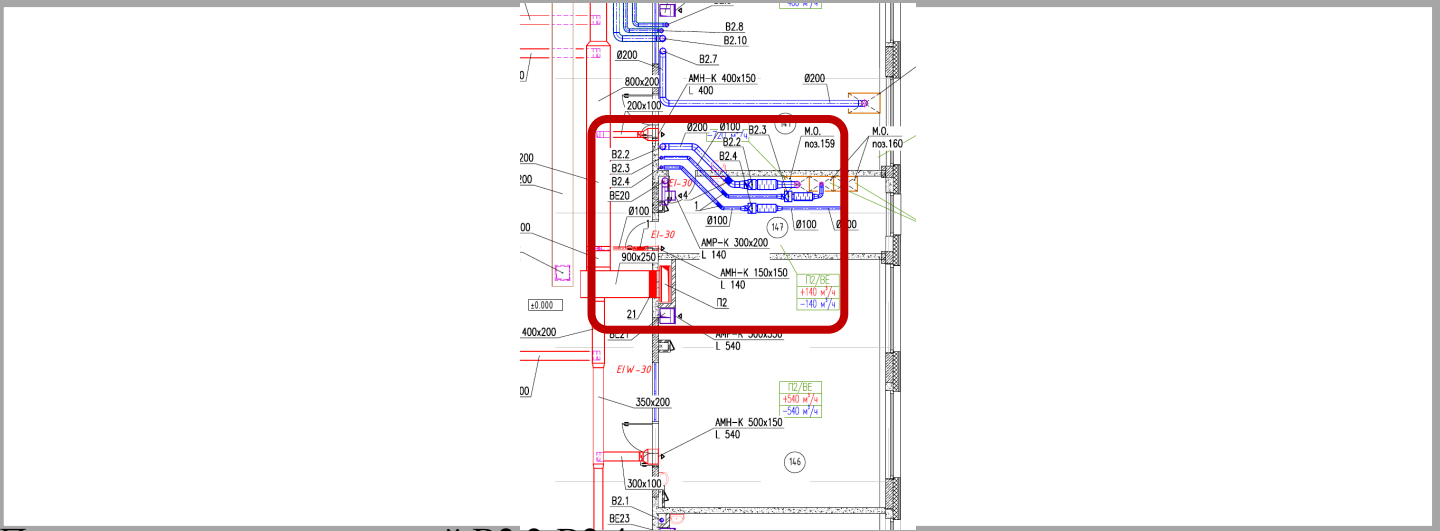


Показана иная группа ветвей В2.2-В2.4 и другая компоновка.

ПД 198 - лист 10

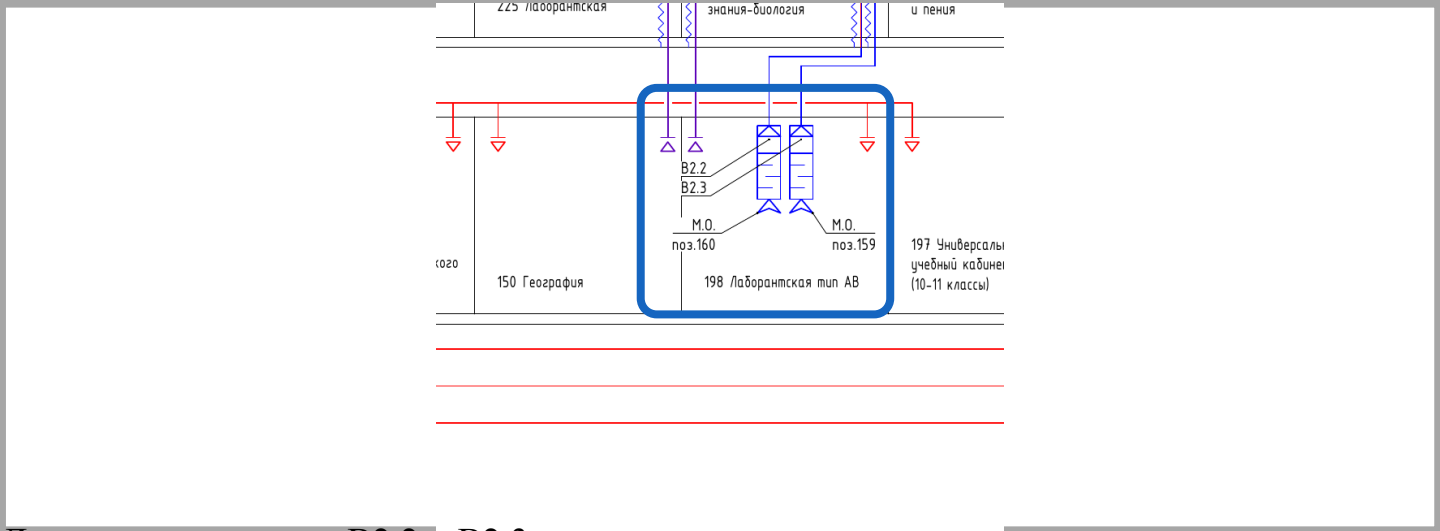

Две проектные ветви В2.2 и В2.3.

РД 198 - лист 4

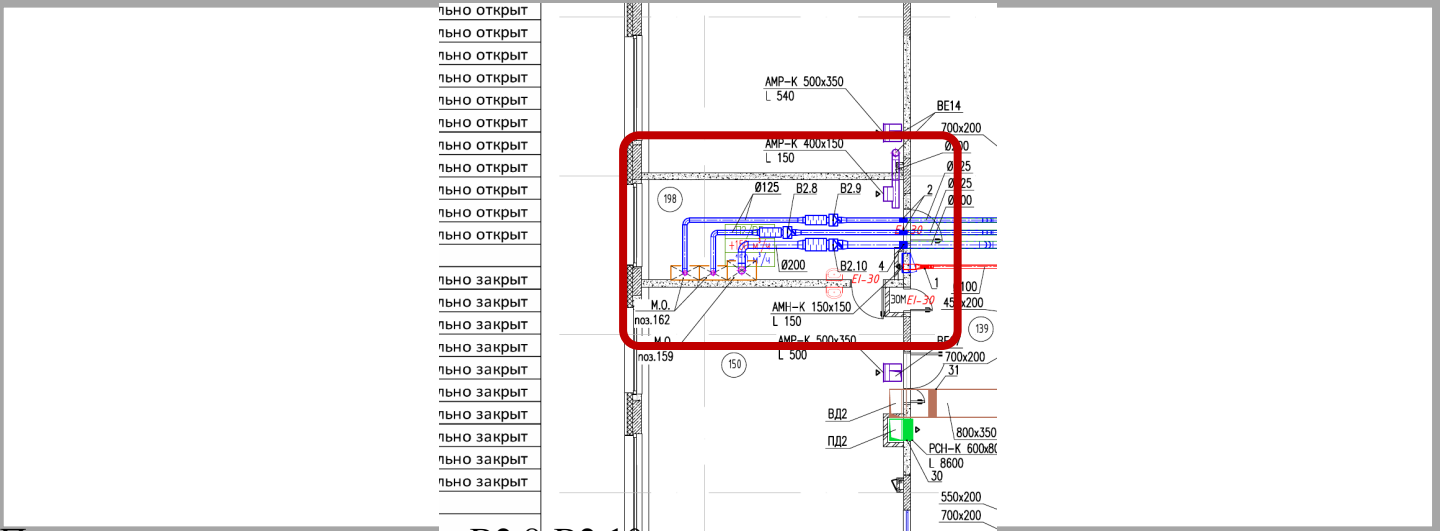

Показана измененная группа В2.8-В2.10.


Вывод

Для помещений 147 и 198 обозначения, число ветвей и компоновка местных вытяжек не совпадают с проектной схемой.

Нарушение 3. Помещение 314


Конфигурация вытяжной вентиляции изменена

ПД - лист 10

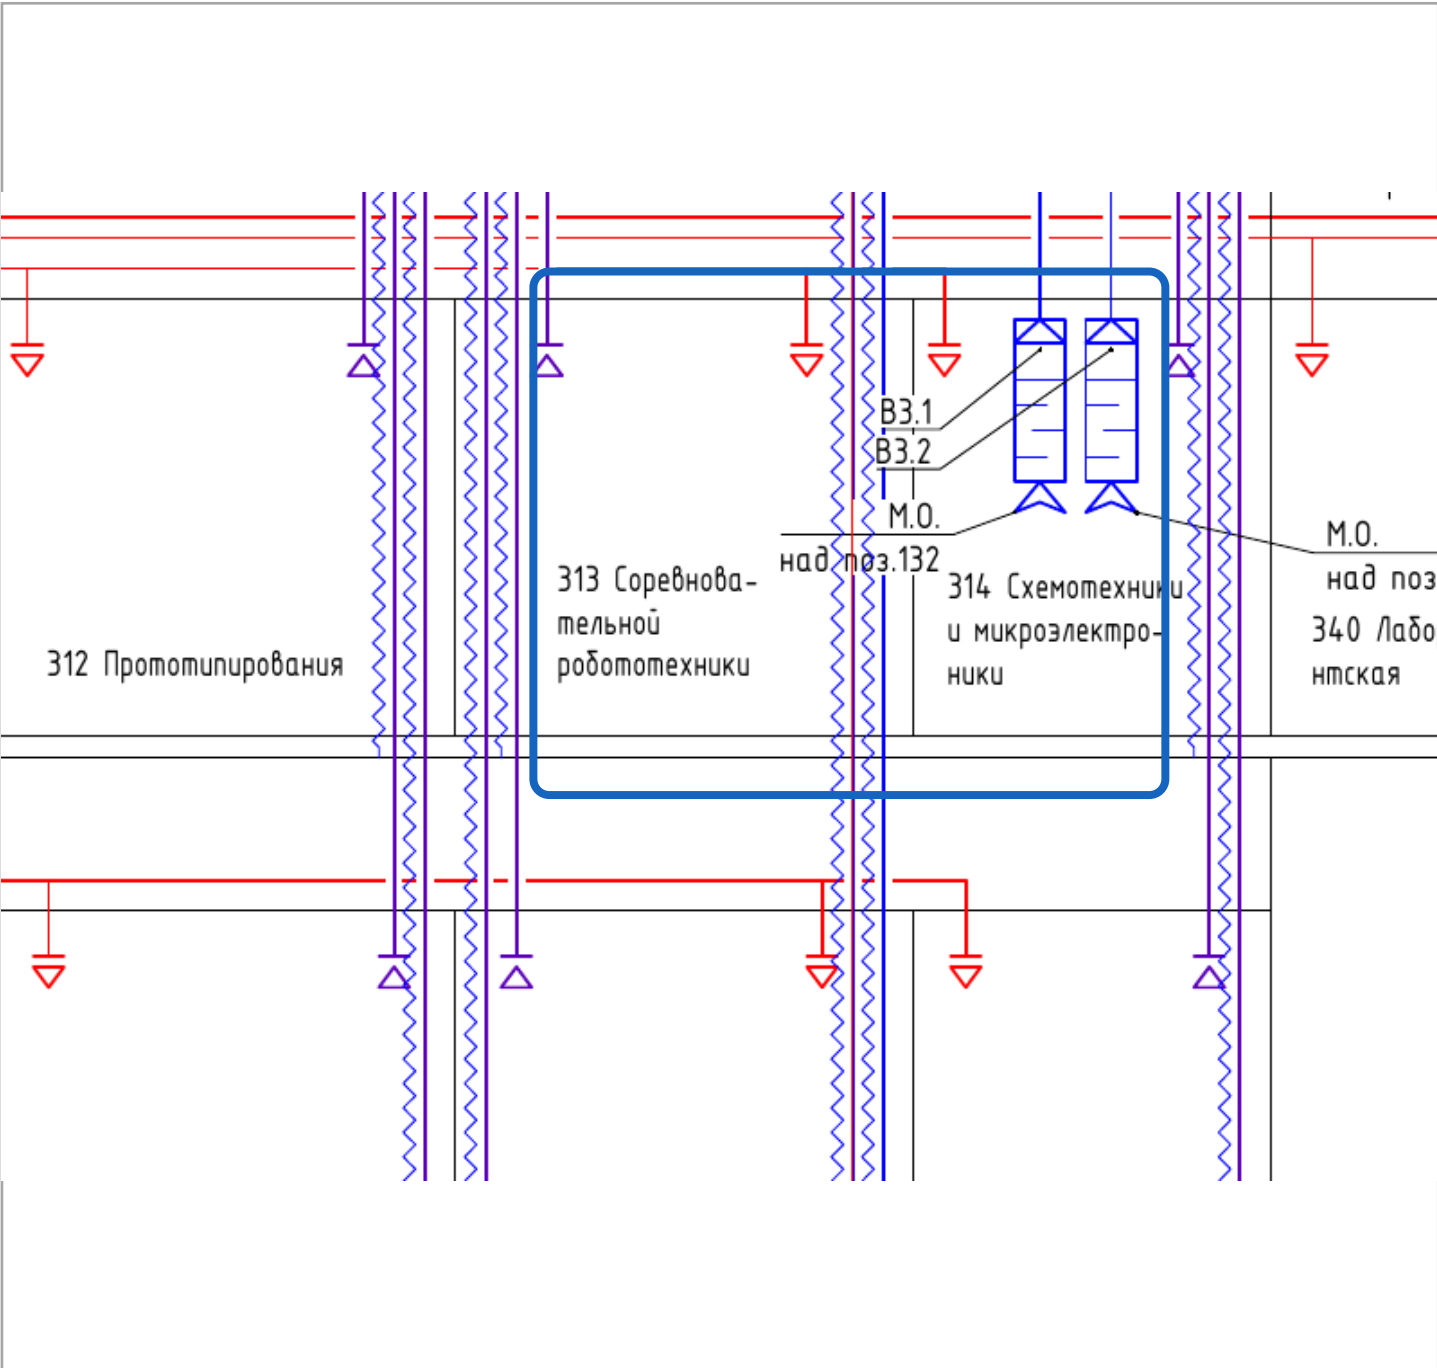

Для помещения 314 предусмотрены две ветви B3.1 и B3.2 к местным отсосам.

РД ОВ1 - лист 6

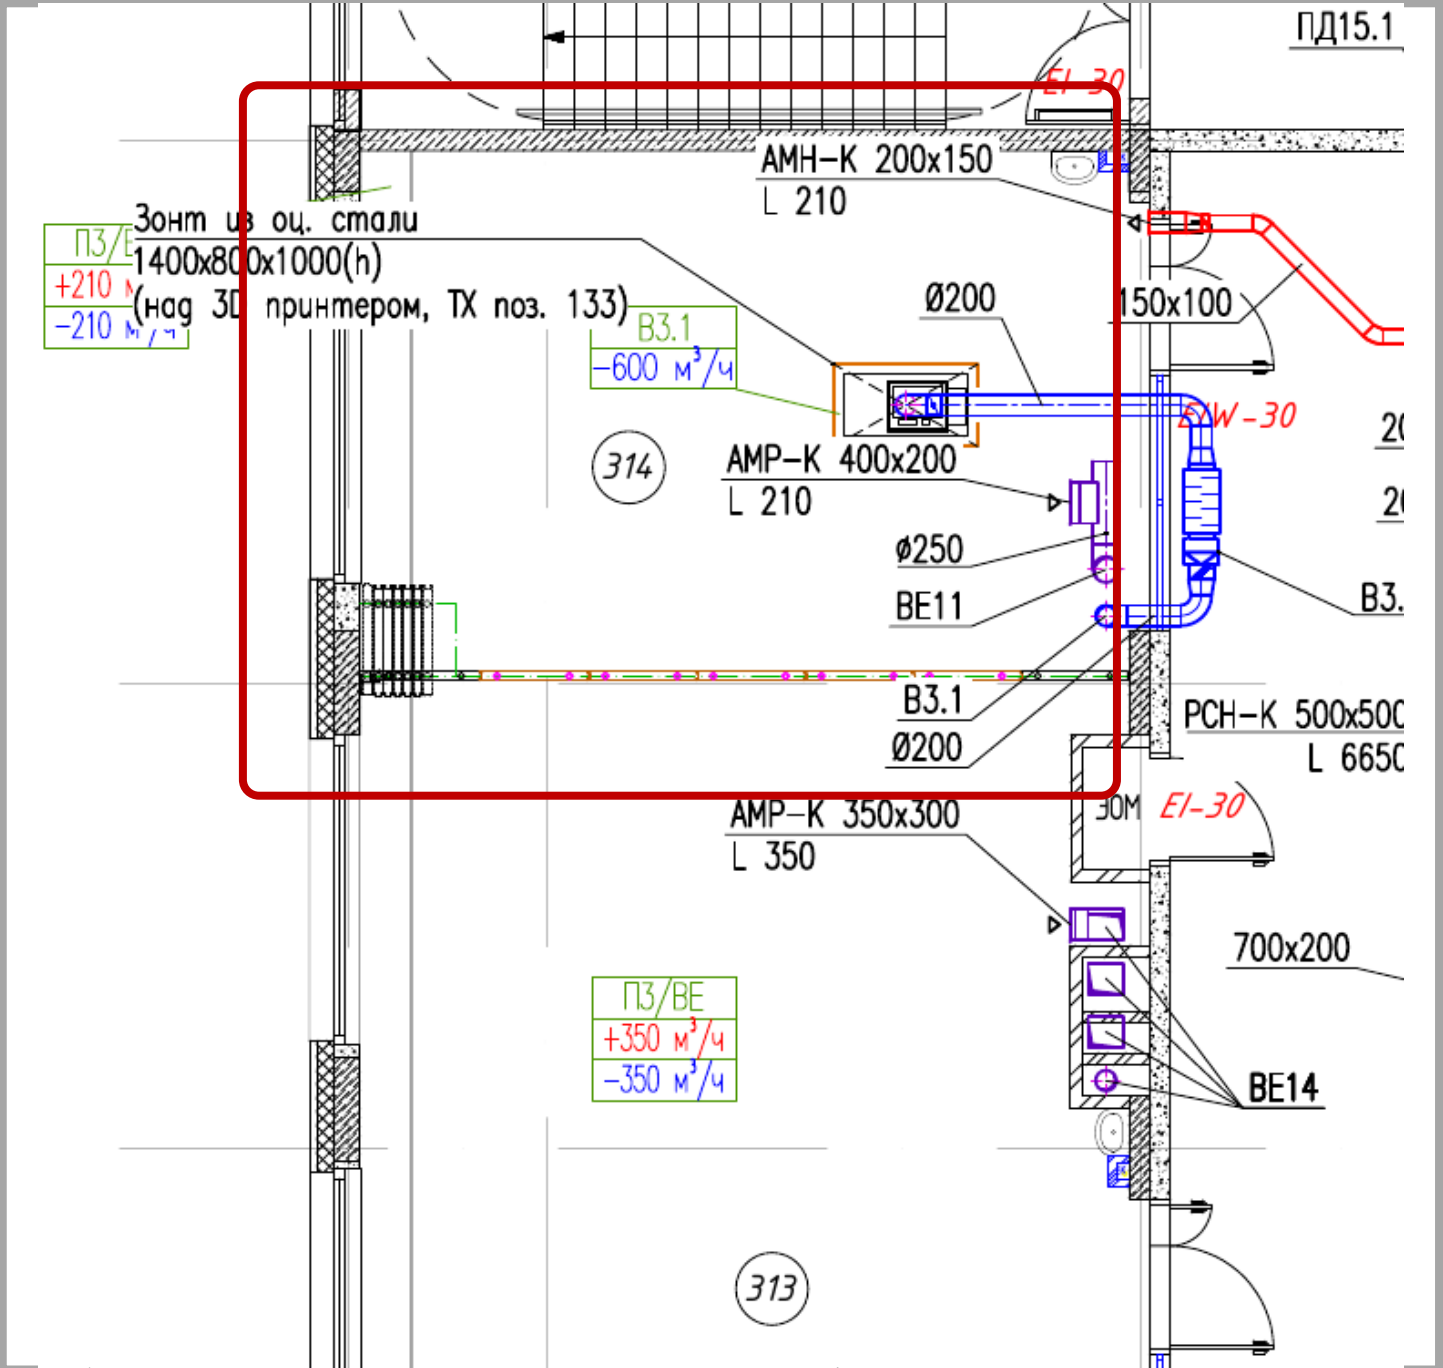

В рабочем плане помещения 314 показана иная конфигурация системы B3.

Вывод

Состав и трассировка вытяжных ветвей помещения 314 отличаются от решения, показанного на листе 10 ПД.